
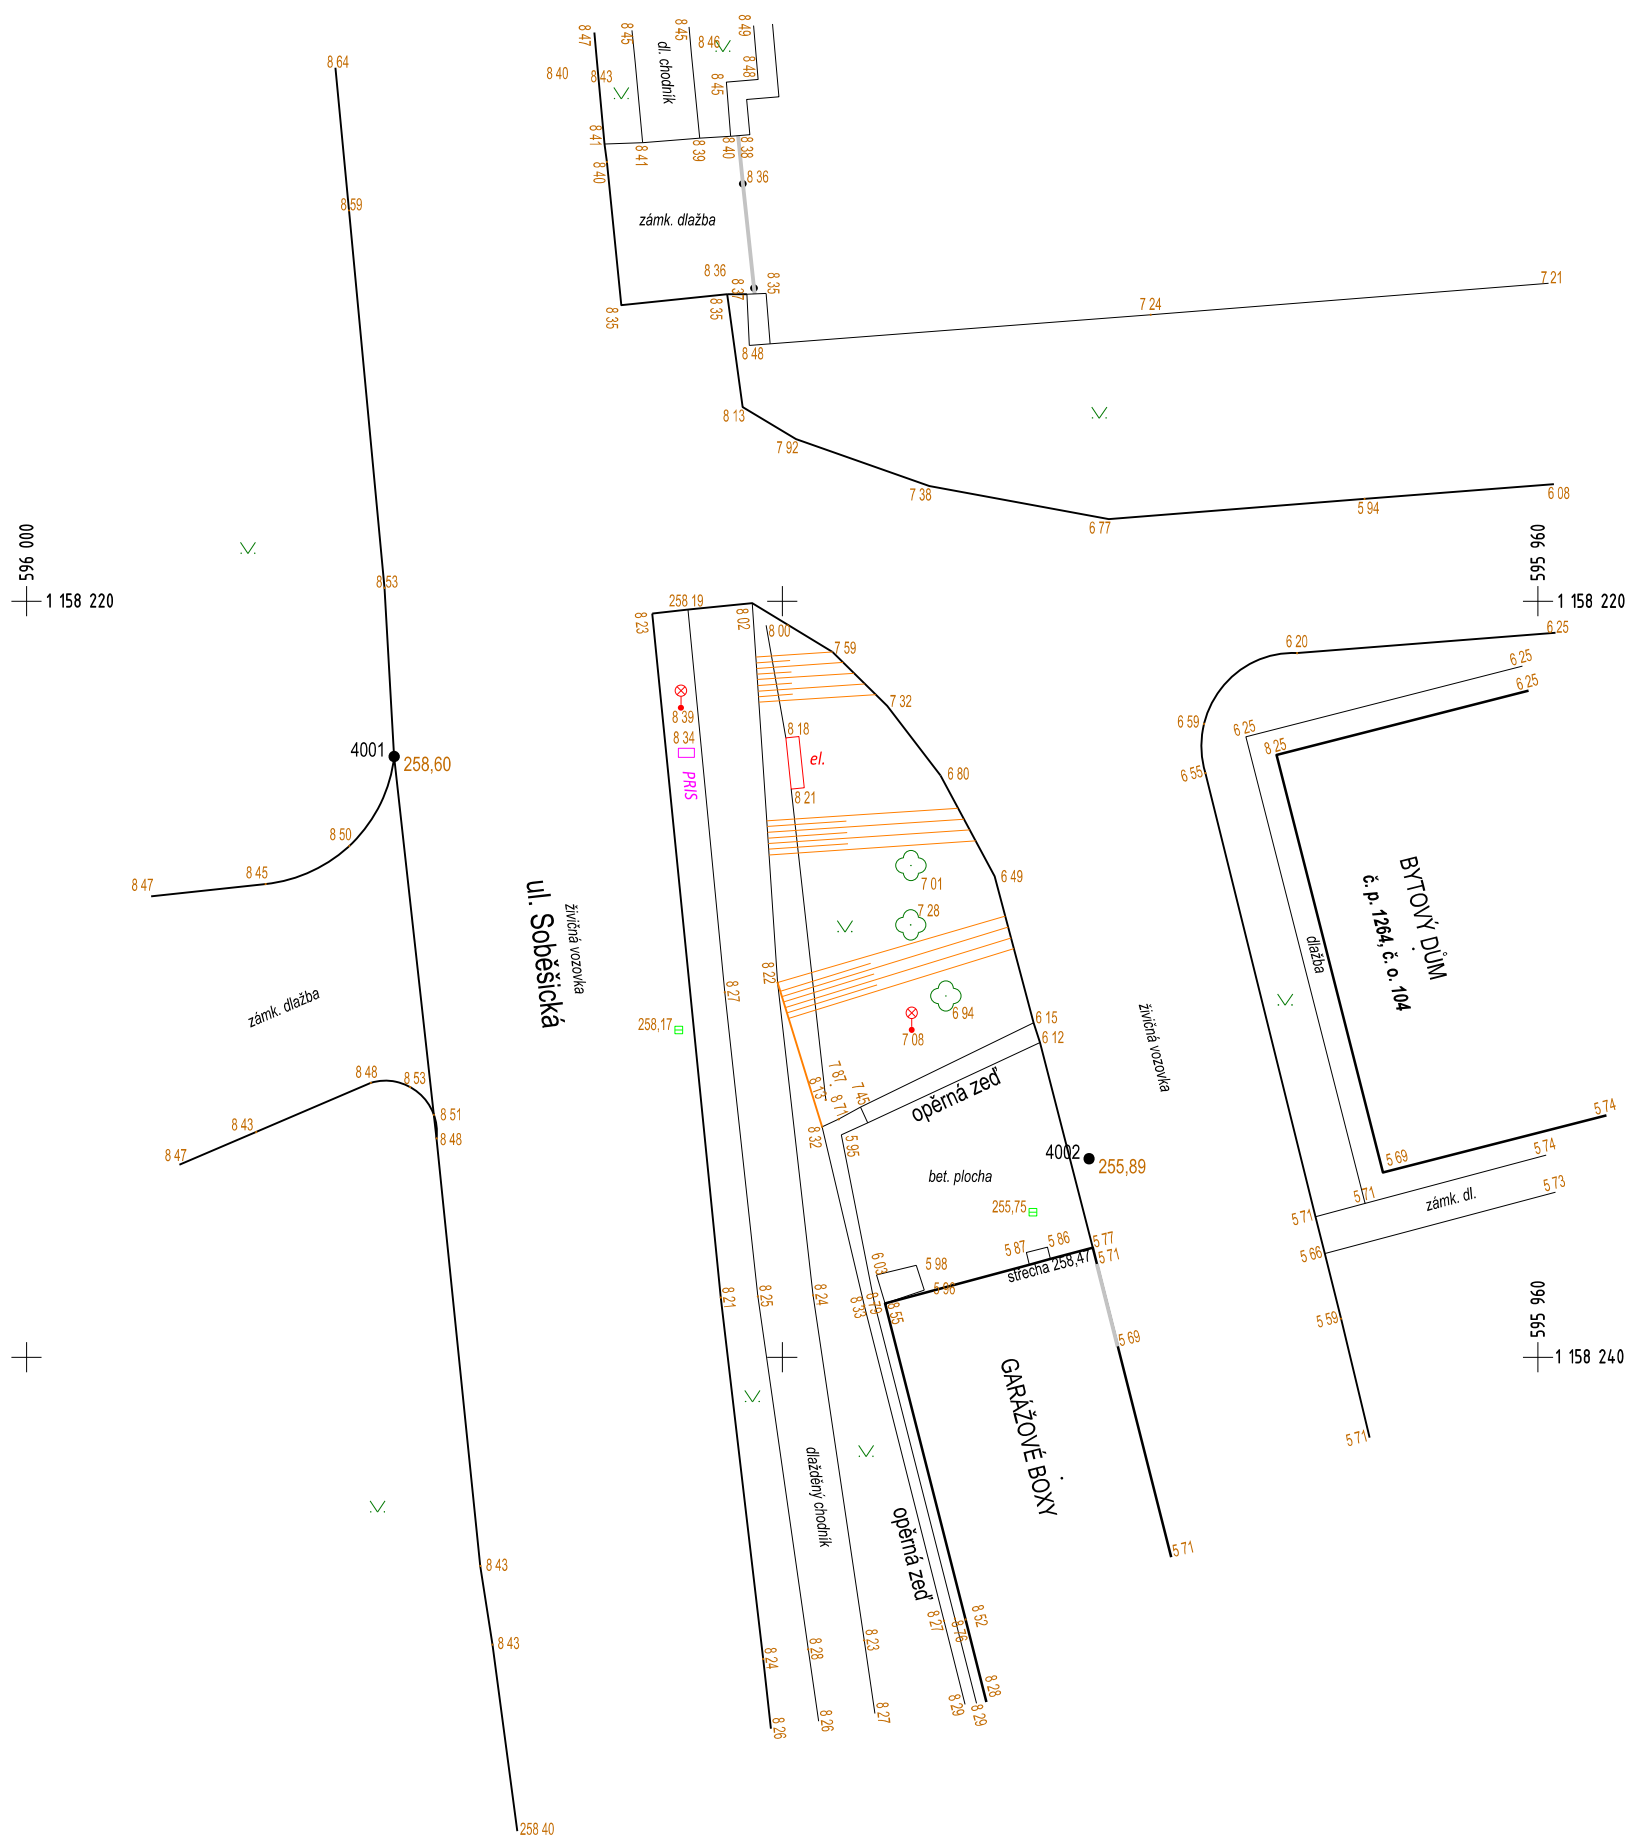


— — — — — Hranice výkresu ÚM  
 = = = = = Hranice ML 1 : 200

## LEGENDA

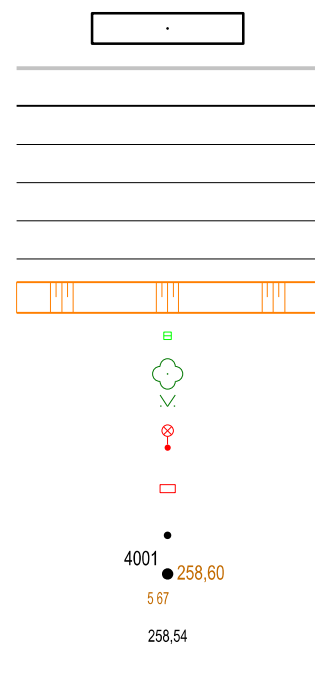

BUDOVA ZDĚNÁ  
VSTUPY DO OBJEKTŮ A POZEMKY  
KOMUNIKACE  
CHODNÍK, ZPEVNĚNÁ PLOCHA, PODEZDÍVKA  
PLOT DRÁTĚNÝ  
ZÁBRADLÍ  
ŽIVÝ PLOT  
TERÉNNÍ STUPEŇ  
VPUST  
JEDNOTLIVÝ STROM  
PARK, OKRASNÁ ZAHRA  
SVÍTIDLO NA STOŽÁRU  
RS VENKOVNÍHO SILOVÉHO VEDENÍ  
SLOUPEK PLOTU  
POMOCNÝ MĚŘICKÝ BOD  
PODROBNÝ VÝŠKOVÝ BOD S VÝŠKOVOU KÓTOU  
VÝŠKOVÁ KÓTA NA STAVEBNÍM OBJEKTU  
SVISLÁ OPĚRNÁ ZEď

|                                                                                   |                     |                   |                                                                         |                        |
|-----------------------------------------------------------------------------------|---------------------|-------------------|-------------------------------------------------------------------------|------------------------|
| Okres: 3702 - Brno-město                                                          |                     |                   | VUT v Brně Fakulta stavební<br>Ústav geodézie<br>Veveří 95, 602 00 Brno |                        |
| Obec, katastrální území: Brno, 610844 - Husovice                                  |                     |                   |                                                                         |                        |
| Souř. systém: S-JTSK                                                              | Výškový systém: Bpv | Tř. přes. map.: 3 |                                                                         |                        |
| <b>Polohopisné a výškopisné zaměření</b><br><br><b>části p.č. 2321/1 a 1361/1</b> |                     |                   | Ověřil                                                                  | <b>Ing. T. Klimeš</b>  |
|                                                                                   |                     |                   | Zpracoval                                                               | <b>Ing. J. Novák</b>   |
|                                                                                   |                     |                   | Měřil                                                                   | <b>Ing. P. Reichel</b> |
|                                                                                   |                     |                   | Vypracoval                                                              | <b>Štěpán Včelák</b>   |
|                                                                                   |                     |                   | Číslo zakázky                                                           | <b>10/2023</b>         |
| <b>Účelová mapa</b>                                                               |                     |                   | Datum                                                                   | <b>1. 9. 2023</b>      |
|                                                                                   |                     |                   | Formát                                                                  | <b>420 × 297 mm</b>    |
|                                                                                   |                     |                   | Měřítko                                                                 | <b>1 : 200</b>         |
|                                                                                   |                     |                   | Příloha č.                                                              | <b>3</b>               |