



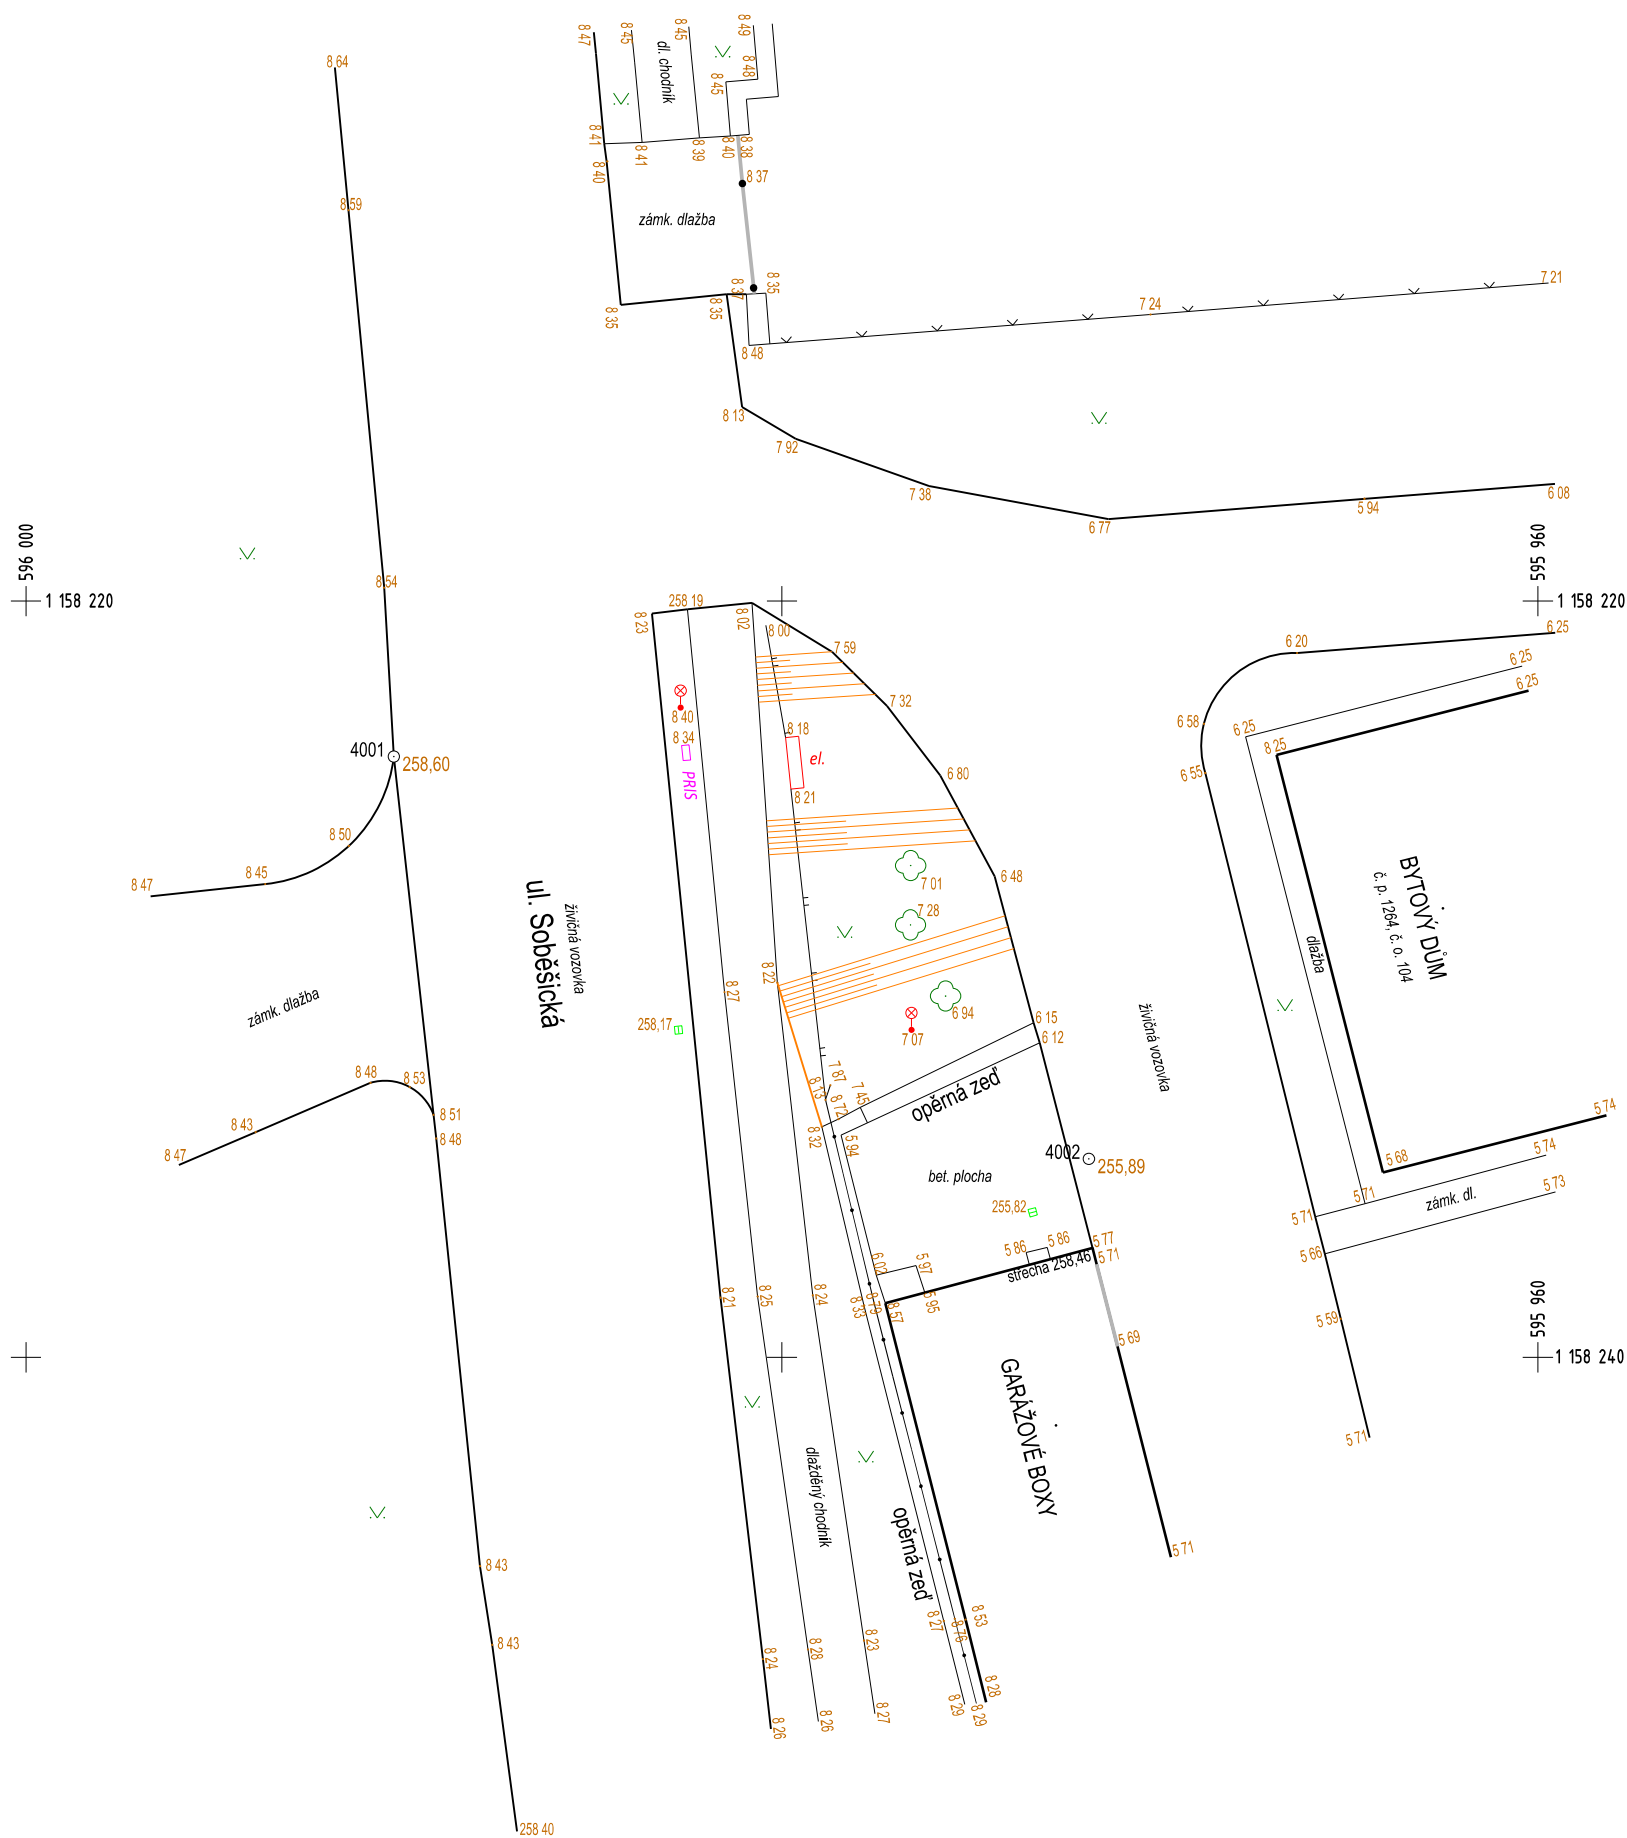

LEGENDA

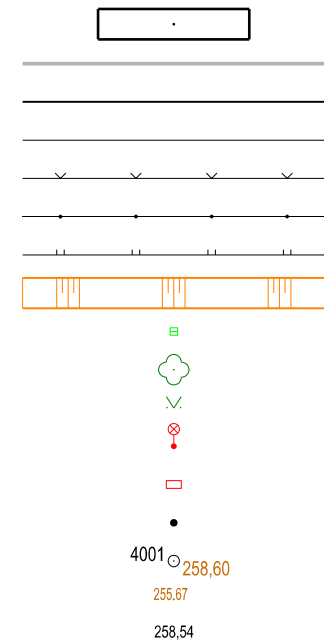

- BUDOVA ZDĚNÁ
- VSTUPY DO OBJEKTŮ A NA POZEMKY
- KOMUNIKACE
- CHODNÍK, ZPEVNĚNÁ PLOCHA, PODEZDÍVKA
- PLOT DRÁTĚNÝ
- ZÁBRADLÍ
- ŽIVÝ PLOT
- TERÉNNÍ STUPEŇ
- VPUST'
- JEDNOTLIVÝ STROM
- PARK, OKRASNÁ ZAHRA
- SVÍTIDLO NA STOŽÁRU
- RS VENKOVNÍHO SILOVÉHO VEDENÍ
- SLOUPEK PLOTU
- POMOCNÝ MĚŘICKÝ BOD
- PODROBNÝ VÝŠKOVÝ BOD S VÝŠKOVOU KÓTOU
- VÝŠKOVÁ KÓTA NA STAVEBNÍM OBJEKTU

|                                                                         |                     |                   |                                                                         |                 |
|-------------------------------------------------------------------------|---------------------|-------------------|-------------------------------------------------------------------------|-----------------|
| Okres: 3702 - Brno-město                                                |                     |                   | VUT v Brně Fakulta stavební<br>Ústav geodézie<br>Veveří 95, 602 00 Brno |                 |
| Obec, katastrální území: Brno, 610844 - Husovice                        |                     |                   |                                                                         |                 |
| Souř. systém: S-JTSK                                                    | Výškový systém: Bpv | Tř. přes. map.: 3 |                                                                         |                 |
| <b>Polohopisné a výškopisné zaměření<br/>části p.č. 2321/1 a 1361/1</b> |                     |                   | Ověřil                                                                  | Ing. T. Klimeš  |
|                                                                         |                     |                   | Zpracoval                                                               | Ing. J. Novák   |
|                                                                         |                     |                   | Měřil                                                                   | Ing. P. Reichel |
|                                                                         |                     |                   | Číslo zakázky                                                           | 10/2023         |
|                                                                         |                     |                   | Datum                                                                   | 1. 9. 2023      |
| <b>Účelová mapa</b>                                                     |                     |                   | Formát                                                                  | 420 × 297 mm    |
|                                                                         |                     |                   | Měřítko                                                                 | 1 : 200         |
|                                                                         |                     |                   | Příloha č.                                                              | 3               |